


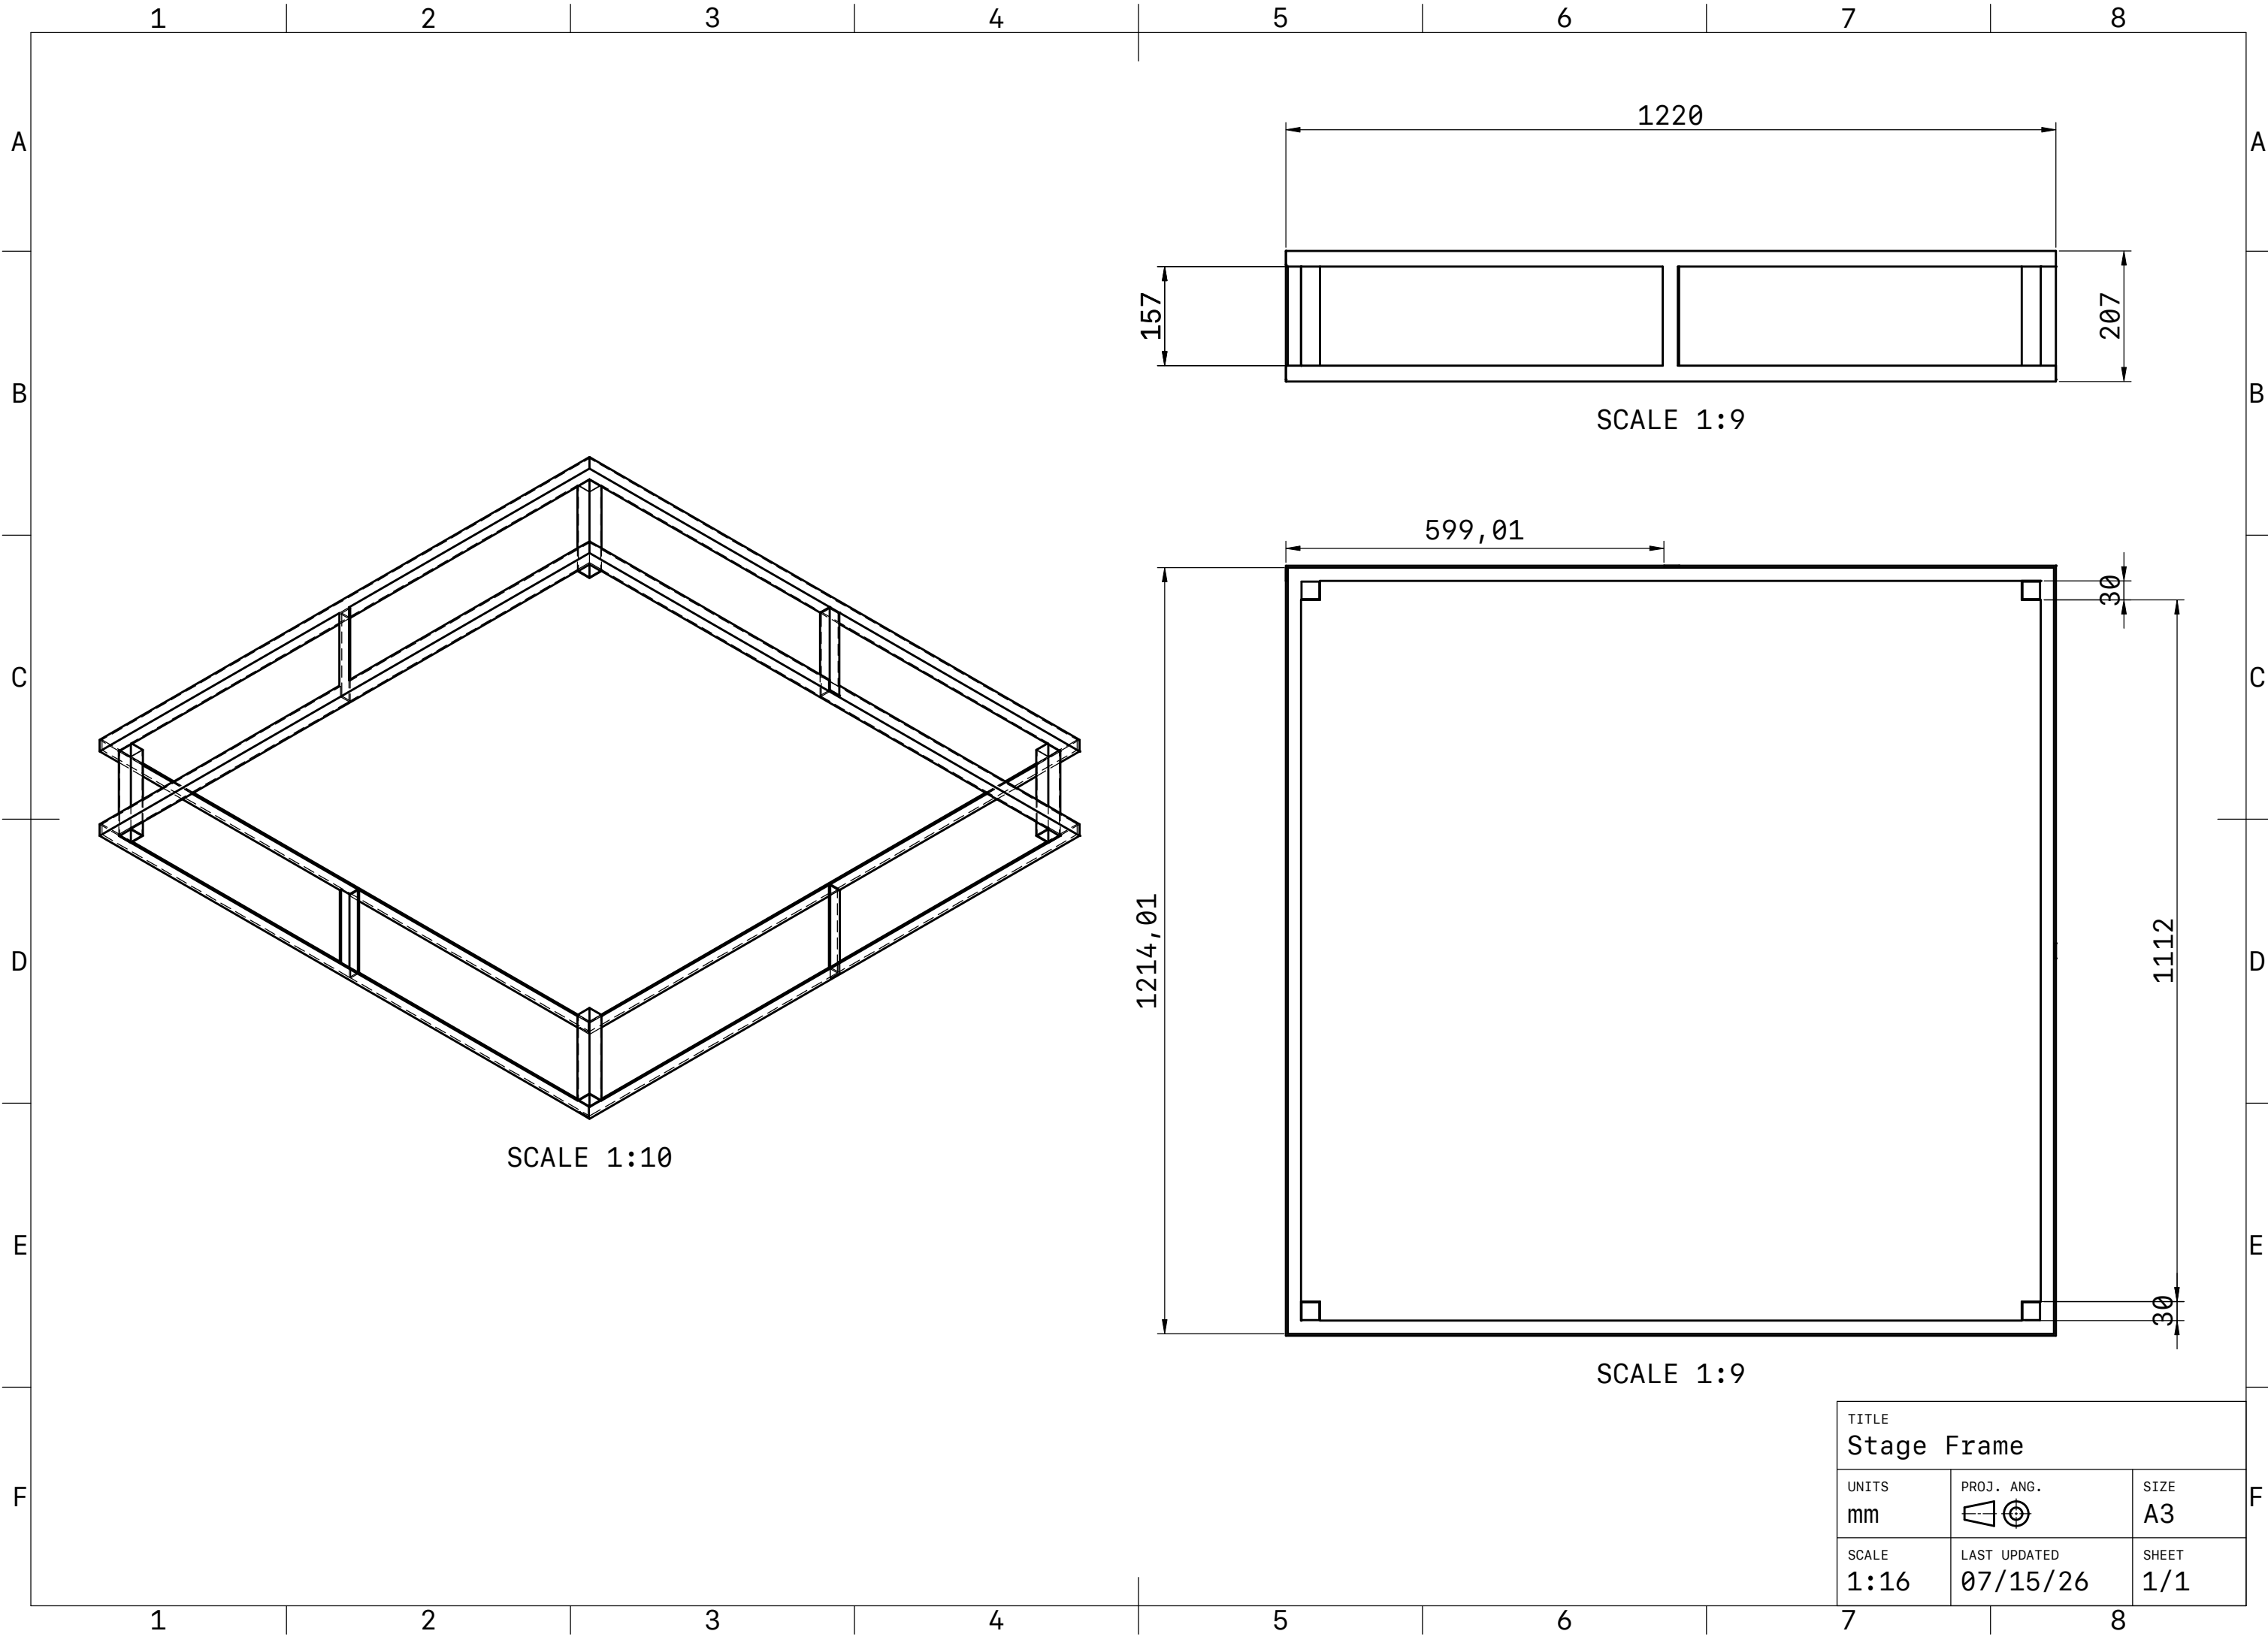

|                      |   |              |
|----------------------|---|--------------|
| TITLE<br>Stage Frame |   |              |
| UNITS<br>mm          | PROJ. ANG.<br> | SIZE<br>A3   |
| SCALE<br>1:16        | LAST UPDATED<br>07/15/26                                                                            | SHEET<br>1/1 |